Depósito de materiales · 100 m²

Planta de distribución y seguridad | Medidas en metros | Uso: depósito seco, sin atención al público ni autoelevadores

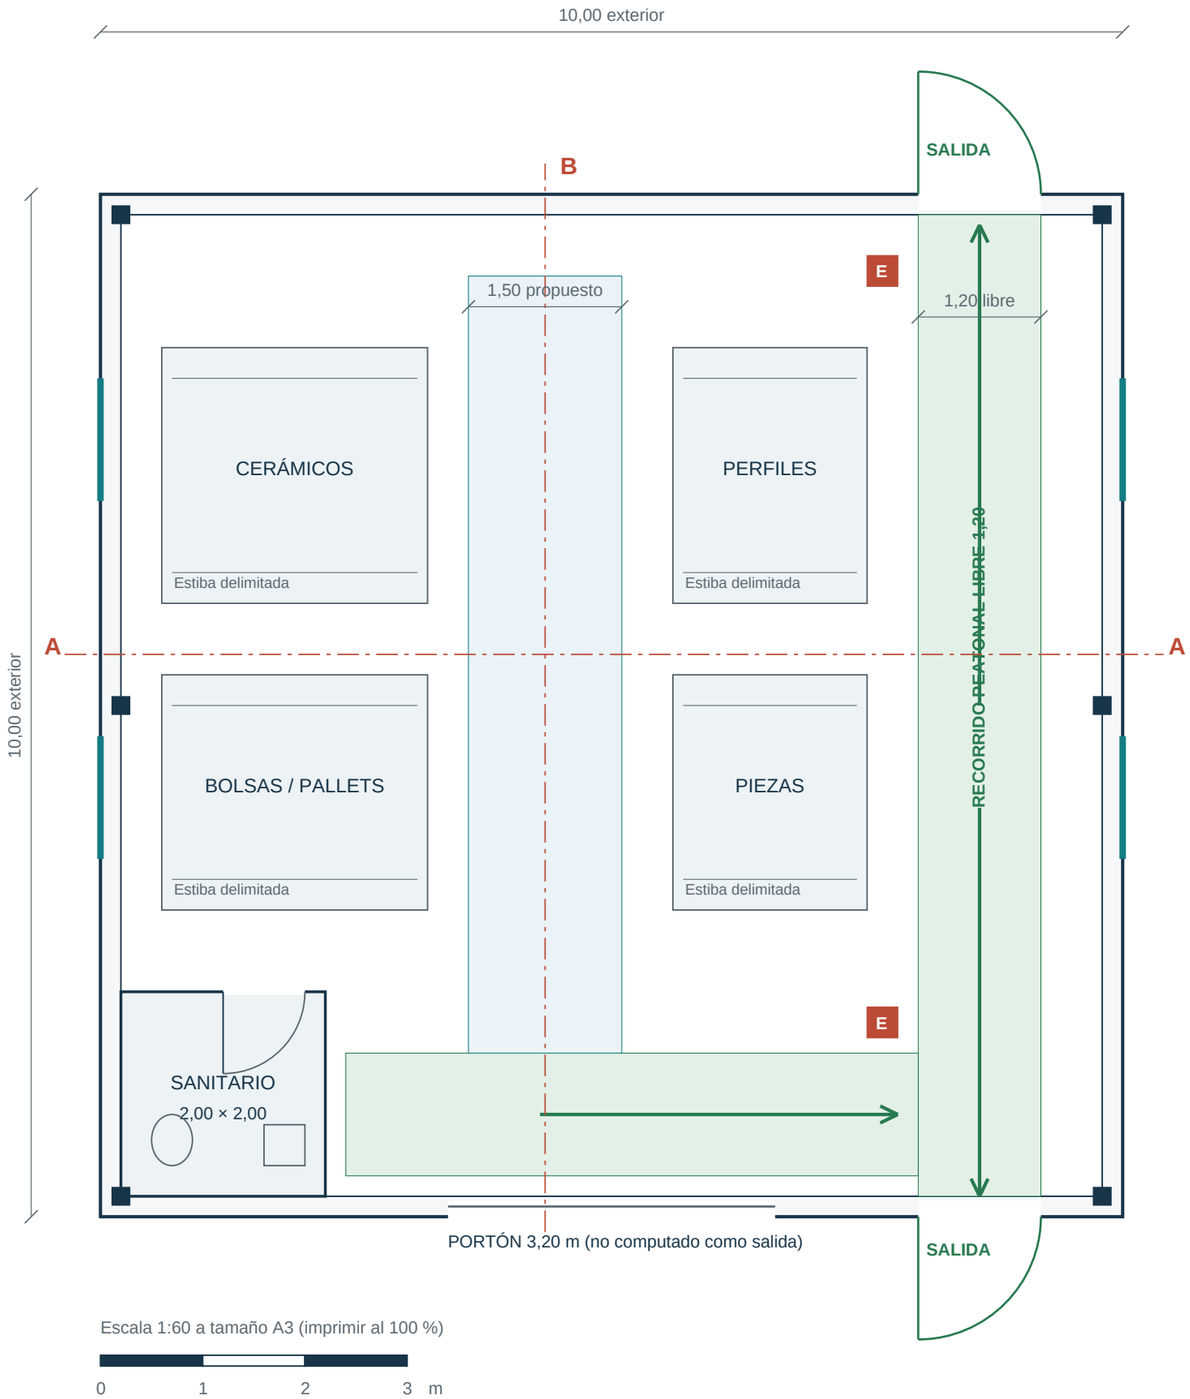

CRITERIOS DE DISTRIBUCIÓN

100,00 m² cubiertos brutos. Cerramiento de referencia: 0,20 m. Superficie interior previa a divisiones: 92,16 m².

Pasillo peatonal: 1,20 m libre propuesto. Pasillo de manejo manual: 1,50 m propuesto. Son decisiones del ejercicio; verificar el ancho con la operación y evacuación reales.

Dos puertas peatonales de 1,20 m libre, abren hacia afuera. Ambas descargan a espacios exteriores seguros y comunicados con la vía pública (condición del emplazamiento).

CONDICIONES DE USO

Ingreso de materiales con zorra manual. Descarga vehicular fuera del edificio; no ingresar camiones ni autoelevadores.

Cemento y yeso sobre pallets secos; cerámicos en embalajes estables; perfiles cortos en soportes con retenes. Barras de 12 m y áridos a granel: patio exterior específico.

Sanitario esquemático para dotación reducida. Ajustar cantidad de artefactos, accesibilidad y servicios a ocupación, normativa y jurisdicción.

LECTURA DEL PLANO

Verde: circulación y salida. Azul: manejo de cargas. E: reserva de ubicación para extintor, a definir por estudio de incendio.

Columnas y cerramientos esquemáticos. No se definen secciones resistentes ni capacidad de estibas.

ANTEPROYECTO DIDÁCTICO | No apto para construir sin cálculo, verificación y aprobación profesional.

Cubierta metálica y fachada principal

Planta de techo y elevación frontal | Escalas indicadas | Pendiente elegida para el ejercicio: 15 % por faldón

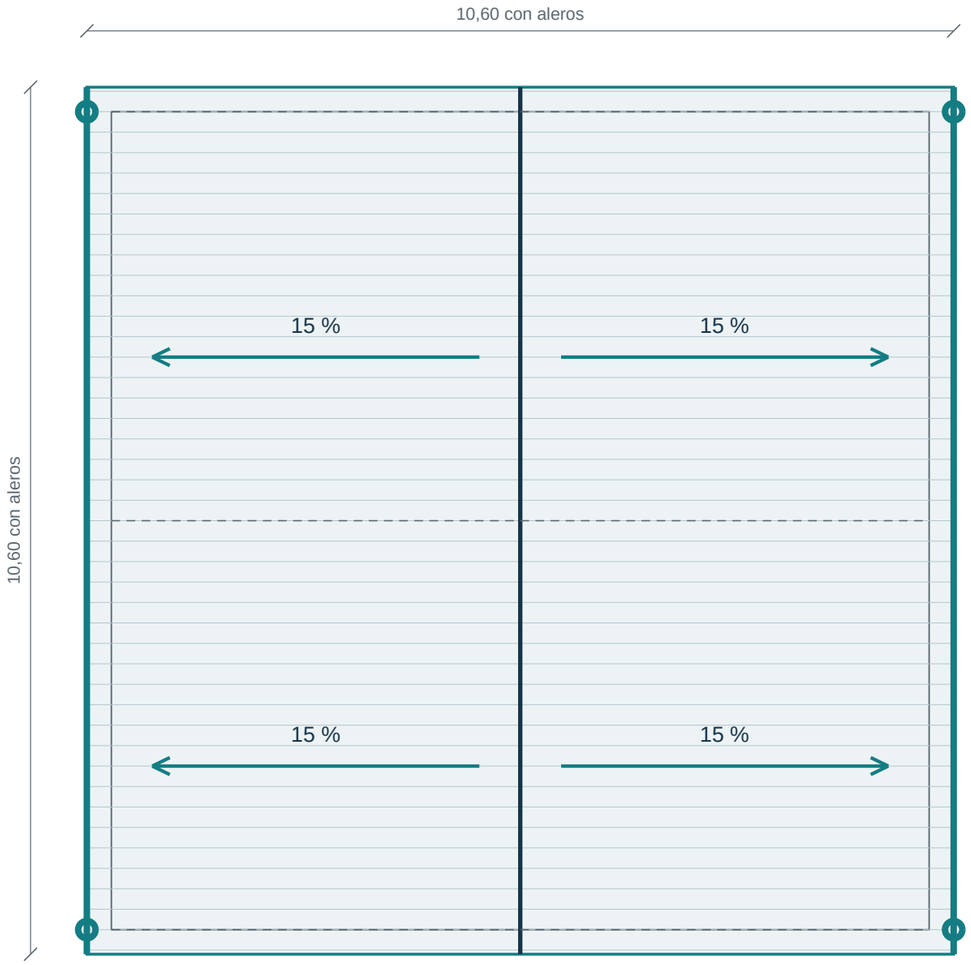

PLANTA DE TECHO | 1:75

Escala 1:75 a tamaño A3 (imprimir al 100 %)

0 1 2 3 m

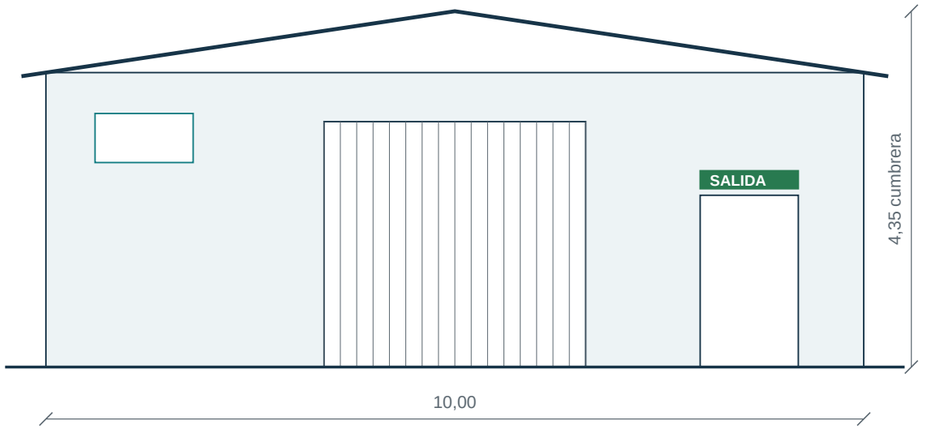

FACHADA PRINCIPAL | 1:75

VENTILACIÓN

Aberturas altas enfrentadas en laterales, con protección de lluvia y malla. Área efectiva a verificar; no sustituye extracción localizada si se genera polvo.

SISTEMA DE CUBIERTA Y AGUA DE LLUVIA

Chapa trapezoidal galvanizada o prepintada, fijaciones con arandelas sellantes, correas metálicas y aislación térmica con control de condensación.

Pendiente 15 %: verificar mínimo admisible, solapes y fijaciones con el fabricante y el cálculo de viento. Alero propuesto: 0,30 m.

Cumbrera longitudinal. Canaletas en ambos laterales y cuatro bajadas indicativas. Dimensionar con lluvia local y superficie tributaria; descargar sin mojar salidas ni veredas.

Pórticos en extremos y eje intermedio: separación longitudinal nominal 5,00 m. Arriostramientos, anclajes y fundaciones por cálculo.

Cortes y materialidad

Corte A-A transversal y corte B-B longitudinal | Escala 1:75 | Niveles referidos al piso terminado ±0,00

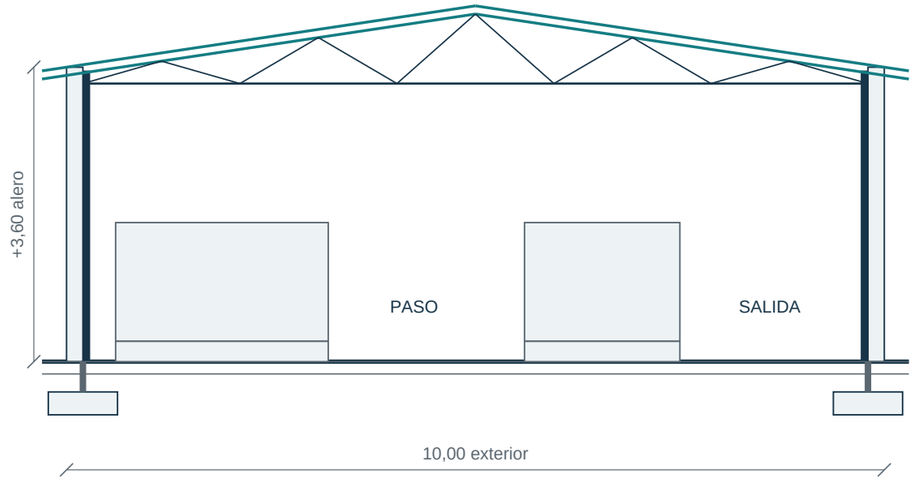

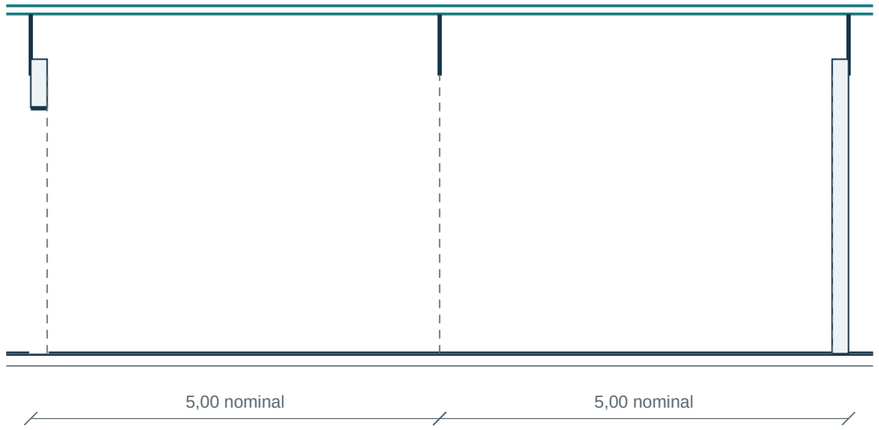

CORTE A-A | 1:75

Escala 1:75 a tamaño A3 (imprimir al 100 %)

0 1 2 3 m

CORTE B-B | 1:75

Corte a x = 4,35 m: nivel de cubierta +4,25 m.

MATERIALES PROPUESTOS

Estructura: acero protegido contra corrosión. Perfiles, uniones y arriostramientos a dimensionar.

Cerramiento: mampostería de 0,20 m de referencia, vinculada a la estructura y verificada frente a acciones horizontales.

Piso: hormigón con terminación antideslizante y juntas. Espesor, armadura y base según suelo, cargas y uso.

Fundaciones dibujadas como símbolo: no expresan dimensiones ejecutivas.

CUBIERTA Y CONFORT

Capas: chapa exterior, sistema de aislación y control de vapor/condensación definido para el clima local.

Altura de alero: +3,60 m; cumbrera: +4,35 m sobre 5,00 m de semiluz. Sección resistente pendiente de cálculo.

Verificar viento, nieve cuando corresponda, sismo, mantenimiento y cargas de instalaciones según reglamentación aplicable.

Iluminación natural alta y luminarias protegidas. Alumbrado de emergencia en rutas y salidas.

USO Y VERIFICACIÓN

Estibas de altura limitada por estabilidad, embalaje y capacidad del soporte; la altura dibujada es ilustrativa.

No cargar sobre cerramientos, no obstruir ventilaciones ni equipos de emergencia. Rotular cargas máximas de racks.

Antes de ejecutar: estudio de suelo, cálculo estructural, proyecto sanitario y eléctrico, incendio y aprobación municipal.

El sanitario, redes y detalles de accesibilidad requieren desarrollo específico.

Seguridad e higiene como criterio de proyecto

Marco argentino de referencia y decisiones verificables | Complemento para lectura del plano y trabajo en clase

ASPECTO	RESPUESTA DEL ANTEPROYECTO	VERIFICACIÓN PARA UN DEPÓSITO REAL
Circulación y egreso	Pasillo peatonal de 1,20 m propuesto y dos salidas de apertura exterior. Portón separado.	Calcular ocupación, medios de escape, recorridos, anchos y descarga segura al exterior. El ancho propuesto no acredita cumplimiento.
Incendio	Dos reservas E para equipos; prohibición de fumar. No se admiten solventes ni combustibles.	Determinar carga de fuego, resistencia al fuego, cantidad/tipo de extintores, ubicación y otras instalaciones según riesgo y jurisdicción.
Estabilidad de cargas	Sectores de estiba delimitados; pesados abajo; bolsas sobre pallets; retenes para perfiles.	Calcular piso y racks, respetar embalajes, alturas, cargas admisibles y anclajes. Inspeccionar estibas y soportes.
Ambiente de trabajo	Ventilación cruzada alta, cubierta aislada, iluminación y control de condensación.	Medir o calcular iluminación y ventilación. Controlar polvo en su origen; establecer extracción y protección respiratoria si corresponde.
Servicios e instalaciones	Sanitario previsto; tablero fuera de circulación, puesta a tierra y protecciones.	Adecuar servicios a dotación, accesibilidad y normativa local. Proyecto eléctrico, medición de puesta a tierra y mantenimiento.
Operación e higiene	Zorra manual, descarga exterior, pasillos sin acopios, limpieza sin dispersar polvo.	Evaluación ergonómica, capacitación, EPP por tarea, botiquín, plan de emergencia, inspecciones y control de plagas.

MARCO NORMATIVO

Ley 19.587 y Decreto 351/79 para el establecimiento, según actividad. Anexo I: características constructivas, provisión de agua, ventilación, iluminación, electricidad, incendio y protección personal; Anexo VII: protección contra incendios.

Durante la construcción: considerar Decreto 911/96 para esa actividad. Completar con normativa provincial y municipal.

ALCANCE DIDÁCTICO

No es una certificación de cumplimiento ni un plano ejecutivo. Las medidas elegidas son propuestas de diseño; cada requisito debe verificarse con uso, dotación, inventario y emplazamiento.

Actividad: justificar cinco decisiones del plano, identificar el material de cada sistema y proponer cómo verificar sus riesgos.

FUENTE OFICIAL CONSULTADA (30/10/2026): Decreto 351/79, texto actualizado y enlaces a anexos.

argentina.gob.ar/normativa/nacional/decreto-351-1979-32030/actualizacion