

PLANTA ARQUITECTÓNICA

Esc. 1:100

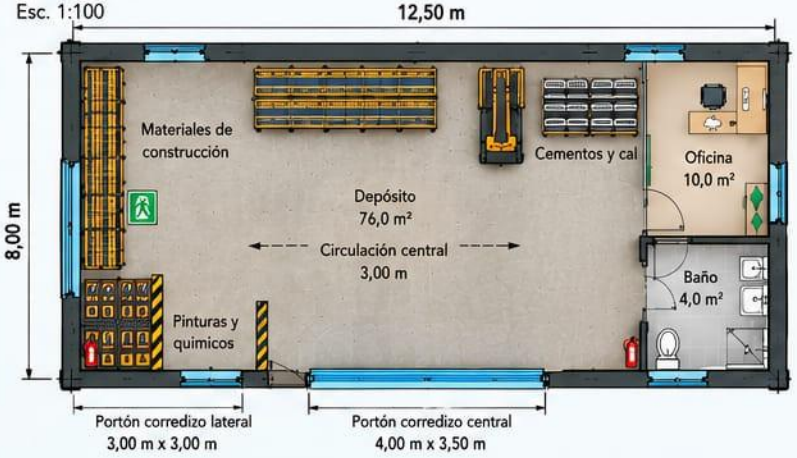

PLANTA DE TECHOS

Esc. 1:100

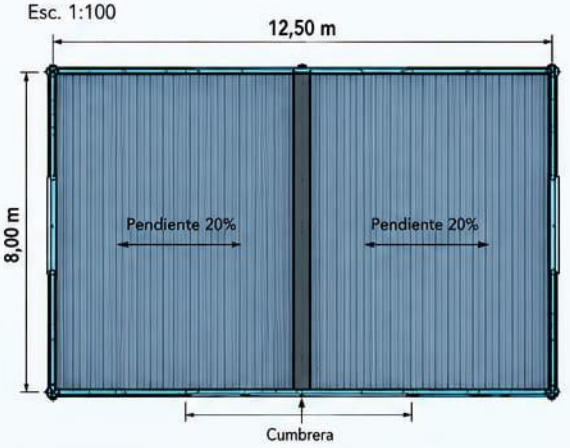

REFERENCIAS

- Muro de mampostería (ladrillo/bloque)
- Tabique de durlock
- Chapa trapezoidal (techo)
- Chapa trapezoidal (muro)
- Canaleta
- Bajada pluvial
- Línea de corte A-A
- Salida de emergencia
- Extintor
- Puerta
- Ventana
- Portón corredizo

CUADRO DE SUPERFICIES


AMBIENTE	SUPERFICIE (m²)
Depósito y almanenamiento	76,0
Oficina	10,0
Baño	4,0
Total cubierta	**100,0**

CUADRO DE ABERTURAS

TIPO	ANCHO (m)	ALTO (m)
Portón corredizo central	4,00	3,50
Portón corredizo lateral	3,00	3,00
Puerta oficina	0,80	2,00
Puerta baño	0,70	2,00
Ventana fachada principal	1,50	0,60
Ventana lateral derecha	1,20	0,60
Ventana oficina	1,00	0,80
Ventana baño	0,60	0,40


FACHADA PRINCIPAL (Sur)

Esc. 1:100

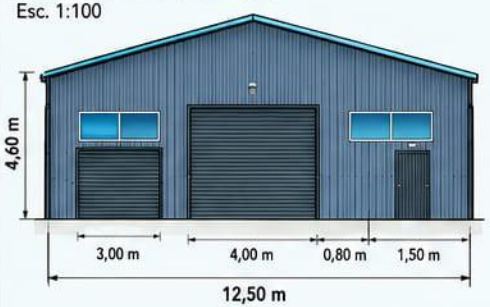


VISTA LATERAL DERECHA (Este)

Esc. 1:100

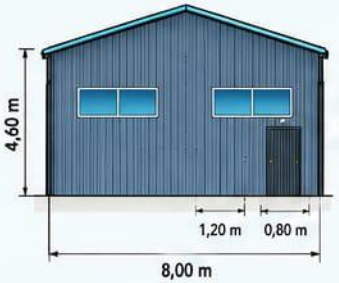


VISTA LATERAL IZQUIERDA (Oeste)

Esc. 1:100

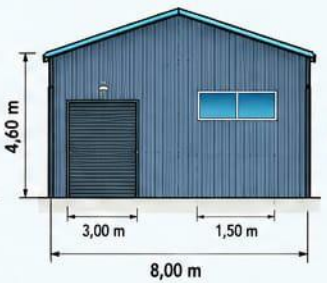

CORTE A-A

Esc. 1:100

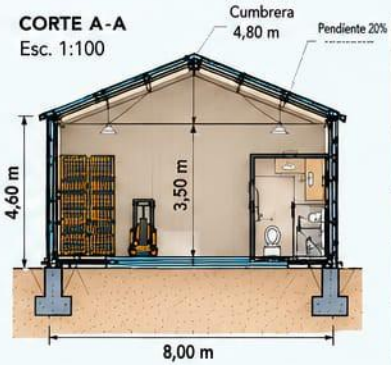

CUADRO DE MATERIALES

PARTE	MATERIAL ELEGIDO	JUSTIFICACIÓN
Cubierta	Chapa trapezoidal galvanizada con aislación térmica	Liviana, resistente y durable.
Estructura	Perfiles de acero	Alta resistencia mecánica y durabilidad.
Muros	Mampostería de bloques + revoque	Buena aislación térmica y acústica.
Piso	Hormigón armado (hormigón H-25)	Resistente al tránsito de maquinaria y materiales.
Carpinterías	Aluminio / chapa	Resistentes y de fácil mantenimiento.
Puertas	Chapa	Acceso seguro y resistente.
Ventanas	Aluminio corredizas	Iluminación y ventilación natural.

MEMORIA DESCRIPTIVA

El proyecto consiste en un depósito para materiales de construcción, pinturas y químicos, con una superficie cubierta de 100 m² (12,50 m x 8,00 m).

Se accede al depósito mediante un portón corredizo central de 4,00 m de ancho y un portón corredizo lateral de 3,00 m, ubicados en la fachada principal. Además, cuenta con un portón corredizo lateral en la pared izquierda y una puerta de acceso en la oficina y el baño.

La estructura es de perfiles de acero y muros de mampostería de bloques con revoque. La cubierta es de chapa trapezoidal galvanizada con aislación térmica. El piso es de hormigón armado de alta resistencia, apto para el tránsito de camiones, maquinaria y materiales.

El diseño prioriza la funcionalidad, la circulación central, la iluminación y ventilación natural, y el cumplimiento de las normas de seguridad e higiene.

NORMAS DE SEGURIDAD E HIGIENE APLICADAS

- ✓ Salidas de emergencia señalizadas y libres de obstáculos.
- ✓ Extintores de incendio ubicados en lugares visibles y accesibles.
- ✓ Iluminación natural y artificial adecuada.
- ✓ Ventilación cruzada en el depósito y en la oficina.
- ✓ Separación del área de pinturas y químicos, con ventilación y señalización.
- ✓ Sector específico para cementos y cal, en pallets y protegidos de la humedad.
- ✓ Circulación interna despejada y señalizada para peatones y vehículos.
- ✓ Protección personal obligatoria (casco, guantes, calzado de seguridad, chaleco reflectivo).
- ✓ Uso de elementos de protección y señalización según normativa.

INSTALACIONES Y DETALLES CONSTRUCTIVOS

- **Instalación eléctrica:** iluminación LED, tomas industriales, tablero principal con térmicas.
- **Instalación sanitaria:** agua fría y caliente, desagües cloacales y pluviales.
- **Sistema de desagüe pluvial:** canaletas y bajadas en ambos laterales.
- **Puertas y portones:** de chapa con guías y herrajes reforzados.
- **Ventanas:** aluminio corredizo con rejas de seguridad.
- **Piso:** hormigón H-25, espesor 10 cm + base granular 15 cm.
- **Muros:** bloques de hormigón, espesor 15 cm, revoque interior y exterior.
- **Cubierta:** chapa trapezoidal + aislación, pendiente 20%.

N

FUENTES CONSULTADAS

- IRAM – Normas de la Construcción.
- Catálogos de chapa galvanizada y perfiles metálicos.
- C.E.T. N.° 33.

DATOS GENERALES

Superficie cubierta: 100 m²
Largo: 12,50 m
Ancho: 8,00 m
Altura lateral: 4,00 m
Altura de cumbrera: 4,80 m
Pendiente de techo: 20%

Escala: 1:100